Zyra kadastrale komunale / Opštinska katastarska kancelarija: Ferizaj

Zona kadastrale / Katastarska zona: Ferizaj

Lloji i njësisë kadastrale / Vrsta katastarske jedinice : Situacion objektit

Nr. i njësisë kadastrale / Br. katastarske jedinice : 03420-1

Numri i lëndës / Broj predmeta:

Shkalla e zvoglimit / Razmera plana : 1:500

Republika e Kosovës

Republika Kosova-Republic of Kosova


Qeveria -Vlada-Government

Ministria e Mjedisit dhe Planifikimit Hapësinor /Ministarstvo Sredine i Prostornog Planiranja/Ministry of Environment and Spatial Planning

AGJENCIA KADASTRALE E KOSOVËS/ KATASTARSKA AGECIJA KOSOVA/ KOSOVA CADASTRAL AGENCY

Pronar: PLAZZA HOLDING L.L.C. 812037465

Koordinatat e Katit 1 të ekzekutuar						
Nr	Y	X	H	Kodi	Përshkrimi	Burimi
1	7511195.440	4693118.621	627.309	Kati 1	Shtëpi-Ndërtesë	PM
2	7511185.423	4693135.748	627.325	Kati 1	Shtëpi-Ndërtesë	PM
3	7511197.748	4693142.917	627.340	Kati 1	Shtëpi-Ndërtesë	PM
4	7511198.231	4693142.084	627.340	Kati 1	Shtëpi-Ndërtesë	PM
5	7511204.591	4693145.814	627.343	Kati 1	Shtëpi-Ndërtesë	PM
6	7511204.124	4693146.650	627.344	Kati 1	Shtëpi-Ndërtesë	PM
7	7511222.596	4693157.383	627.347	Kati 1	Shtëpi-Ndërtesë	PM
8	7511232.545	4693140.287	627.331	Kati 1	Shtëpi-Ndërtesë	PM

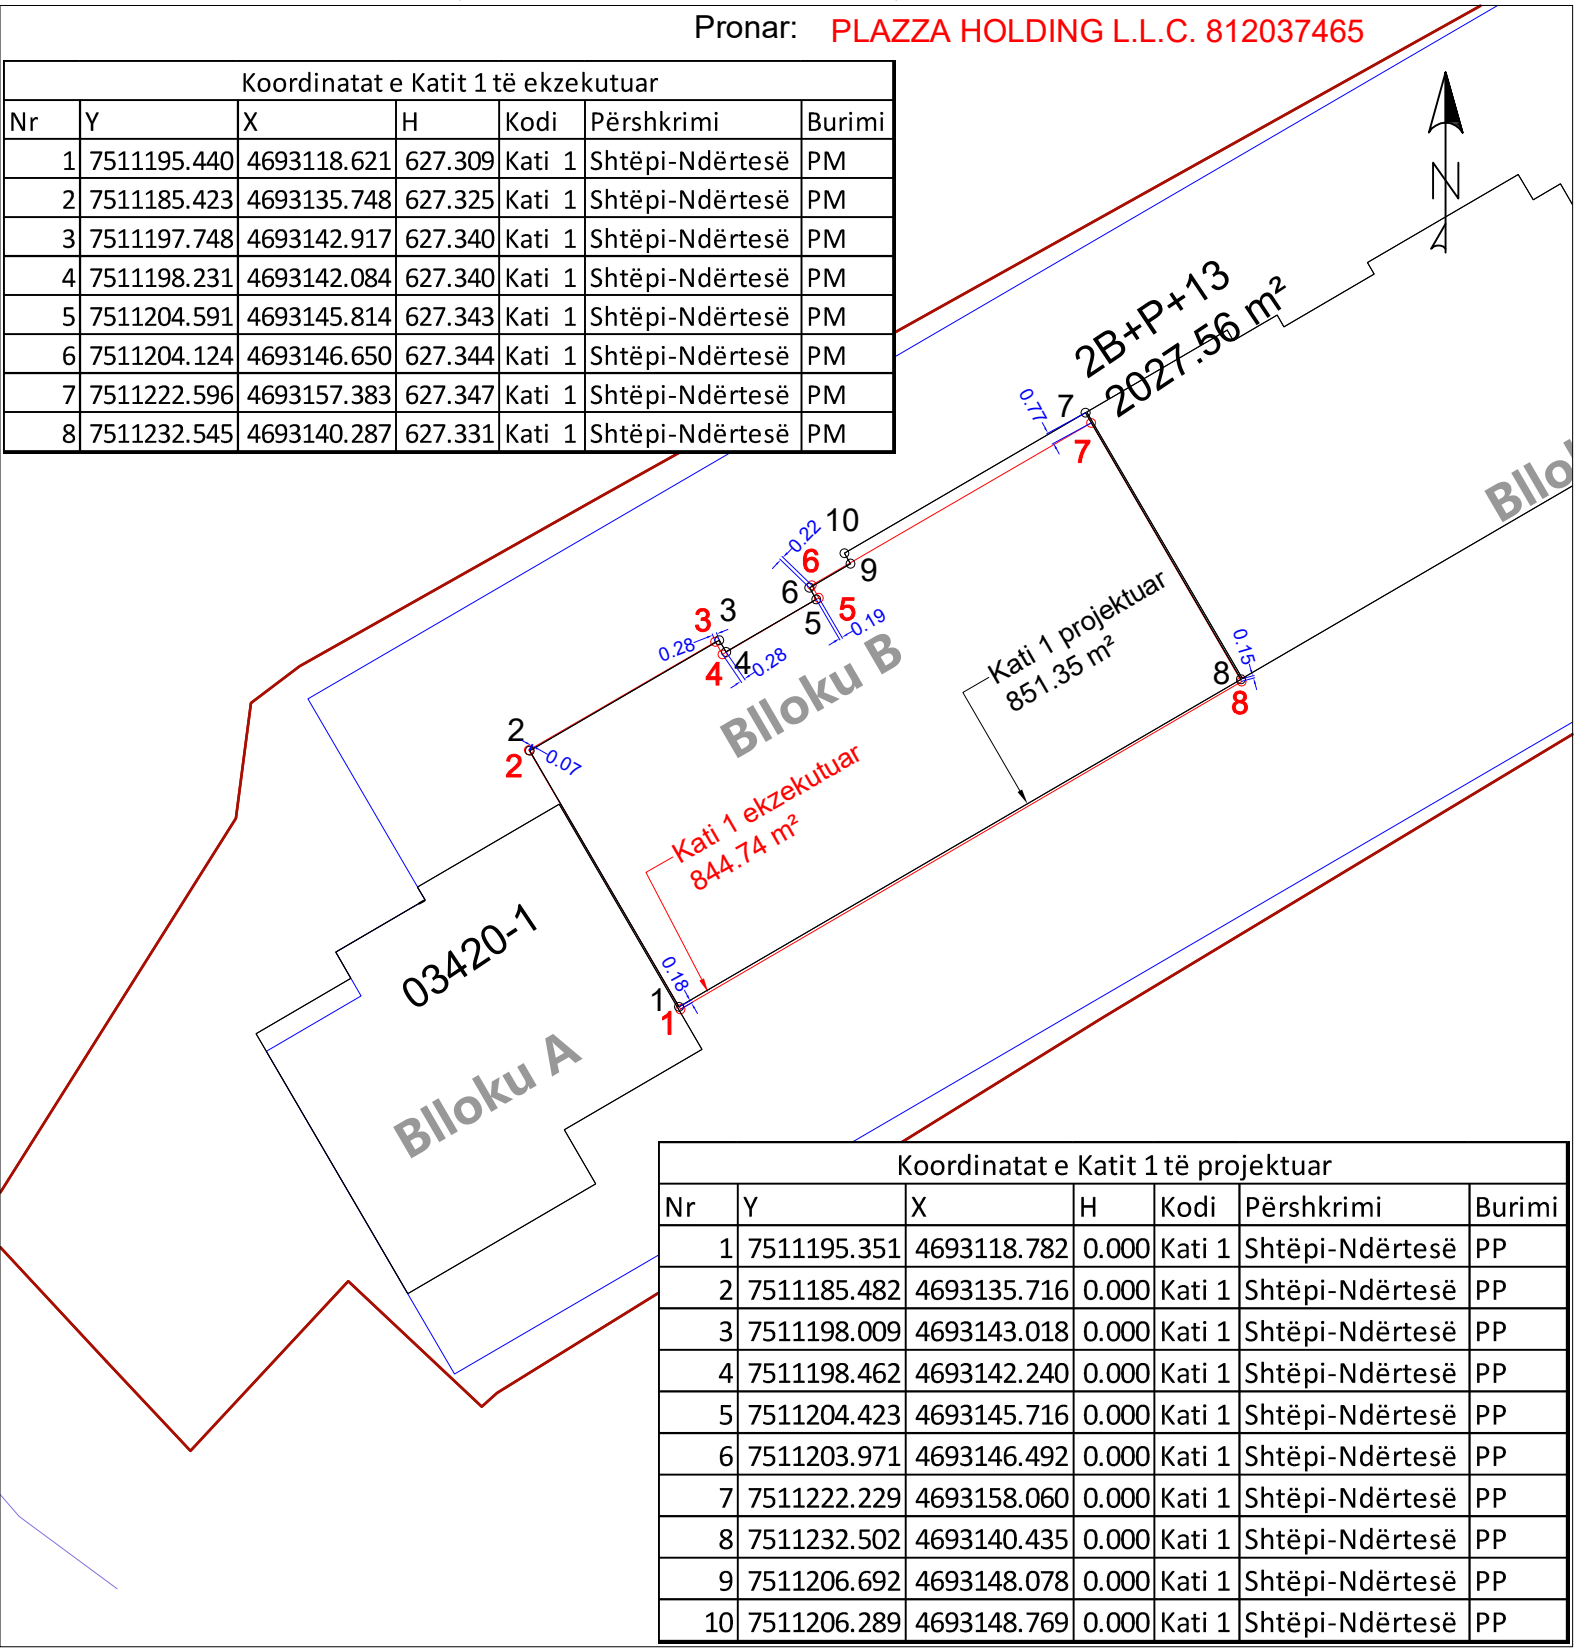

Koordinatat e Katit 1 të projektuar						
Nr	Y	X	H	Kodi	Përshkrimi	Burimi
1	7511195.351	4693118.782	0.000	Kati 1	Shtëpi-Ndërtesë	PP
2	7511185.482	4693135.716	0.000	Kati 1	Shtëpi-Ndërtesë	PP
3	7511198.009	4693143.018	0.000	Kati 1	Shtëpi-Ndërtesë	PP
4	7511198.462	4693142.240	0.000	Kati 1	Shtëpi-Ndërtesë	PP
5	7511204.423	4693145.716	0.000	Kati 1	Shtëpi-Ndërtesë	PP
6	7511203.971	4693146.492	0.000	Kati 1	Shtëpi-Ndërtesë	PP
7	7511222.229	4693158.060	0.000	Kati 1	Shtëpi-Ndërtesë	PP
8	7511232.502	4693140.435	0.000	Kati 1	Shtëpi-Ndërtesë	PP
9	7511206.692	4693148.078	0.000	Kati 1	Shtëpi-Ndërtesë	PP
10	7511206.289	4693148.769	0.000	Kati 1	Shtëpi-Ndërtesë	PP

Rilevoi / Snimio: Liridon Sejdiu

(emri dhe mbiemri i gjeodetit/kompanisë/ ime i prezime geodeta/ kompanije)

Nr. i licencës / Br. licence: 140

Nënshkrimi / Potpis:

Data e rilevimit / Datum snimanja: 10/06/2026

Etazha: Kati 1

V.V.

Nënshkrimi / Potpis:

Data e aprovimit / Datum usvajanja: