

Zyra kadastrale komunale / Opštinska katastarska kancelarija: Ferizaj

Zona kadastrale / Katastarska zona: Ferizaj

Lloji i njësisë kadastrale / Vrsta katastarske jedinice : Situacion objektit




Nr. i njësisë kadastrale / Br. katastarske jedinice : 03420-1

Numri i lëndës / Broj predmeta:

Shkalla e zvoglimit / Razmera plana : 1:500

Republika e Kosovës
Republika Kosova-Republic of Kosovo
Qeveria -Vlada-Government
Ministria e Mjedisit dhe Planifikimit Hapësinor /Ministarstvo Sredine i Prostornog Planiranja/Ministry of Environment and Spatial Planning
AGJENCIA KADASTRALE E KOSOVËS/ KATASTARSKA AGENCIJA KOSOVA/ KOSOVA CADASTRAL AGENCY

Pronar: PLAZZA HOLDING L.L.C. 812037465

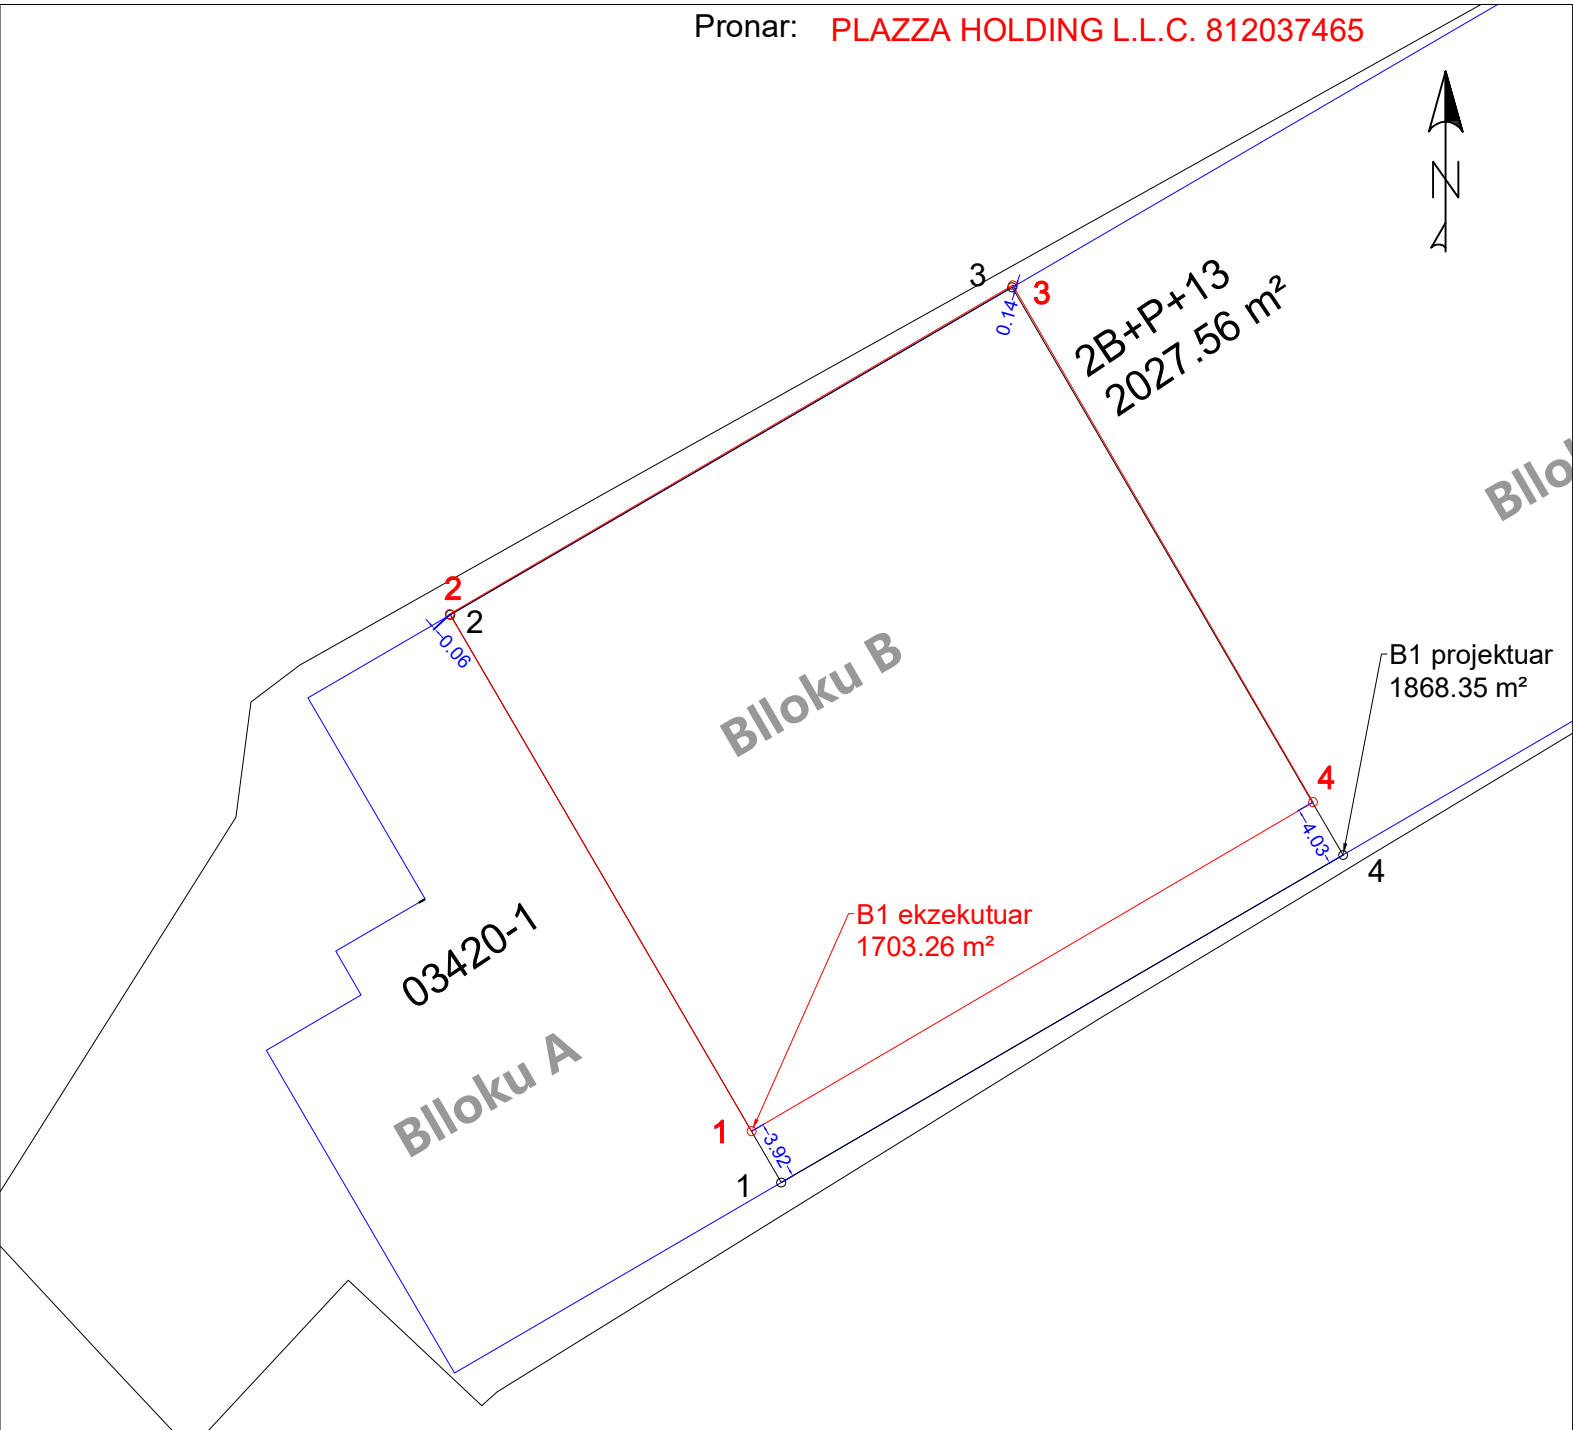

Koordinatat e Katit -1B të projektuar						
Nr	Y	X	H	Kodi	Përshkrimi	Burimi
1	7511202.106	4693107.094	0.000	Kati -1B	Shtëpi-Ndërtesë	PP
2	7511180.227	4693144.633	0.000	Kati -1B	Shtëpi-Ndërtesë	PP
3	7511217.377	4693166.286	0.000	Kati -1B	Shtëpi-Ndërtesë	PP
4	7511239.257	4693128.747	0.000	Kati -1B	Shtëpi-Ndërtesë	PP

Koordinatat e Katit -1B të ekzekutuar						
Nr	Y	X	H	Kodi	Përshkrimi	Burimi
1	7511200.153	4693110.493	620.989	Kati -1B	Shtëpi-Ndërtesë	PM
2	7511180.187	4693144.676	621.060	Kati -1B	Shtëpi-Ndërtesë	PM
3	7511217.416	4693166.416	621.024	Kati -1B	Shtëpi-Ndërtesë	PM
4	7511237.265	4693132.248	621.036	Kati -1B	Shtëpi-Ndërtesë	PM

Rilevoi / Snimio: Liridon Sejdiu
(emri dhe mbiemri i gjeodetit/kompanisë/ ime i prezime geodeta/ kompanije)

Nr. i licencës / Br. licence: 140

Nënshkrimi / Potpis:

Data e rilevimit / Datum snimanja: 29/10/2025

Etazha: Kati -1B

Nënshkrimi / Potpis:

Data e aprovimit / Datum usvajanja: