Zyra kadastrale komunale / Opštinska katastarska kancelarija: Ferizaj

Zona kadastrale / Katastarska zona: Ferizaj

Lloji i njësisë kadastrale / Vrsta katastarske jedinice : Situacion objektit

Nr. i njësisë kadastrale / Br. katastarske jedinice : 03420-1

Numri i lëndës / Broj predmeta:

Shkalla e zvoglimit / Razmera plana : 1:500

Republika e Kosovës

Republika Kosova-Republic of Kosova


Qeveria -Vlada-Government

Ministria e Mjedisit dhe Planifikimit Hapësinor /Ministarstvo Sredine i Prostornog Planiranja/Ministry of Environment and Spatial Planning

AGJENCIA KADASTRALE E KOSOVËS/ KATASTARSKA AGECIJA KOSOVA/ KOSOVA CADASTRAL AGENCY

Pronar: PLAZZA HOLDING L.L.C. 812037465

Koordinatat e Katit - Pllaka mbi Bodrum të projektuar						
Nr	Y	X	H	Kodi	Përshkrimi	Burimi
1	7511202.106	4693107.094	0.000	Kati-Pllaka mbi Bodrum	Shtëpi-Ndërtesë	PP
2	7511180.227	4693144.633	0.000	Kati-Pllaka mbi Bodrum	Shtëpi-Ndërtesë	PP
3	7511217.377	4693166.286	0.000	Kati-Pllaka mbi Bodrum	Shtëpi-Ndërtesë	PP
4	7511239.257	4693128.747	0.000	Kati-Pllaka mbi Bodrum	Shtëpi-Ndërtesë	PP

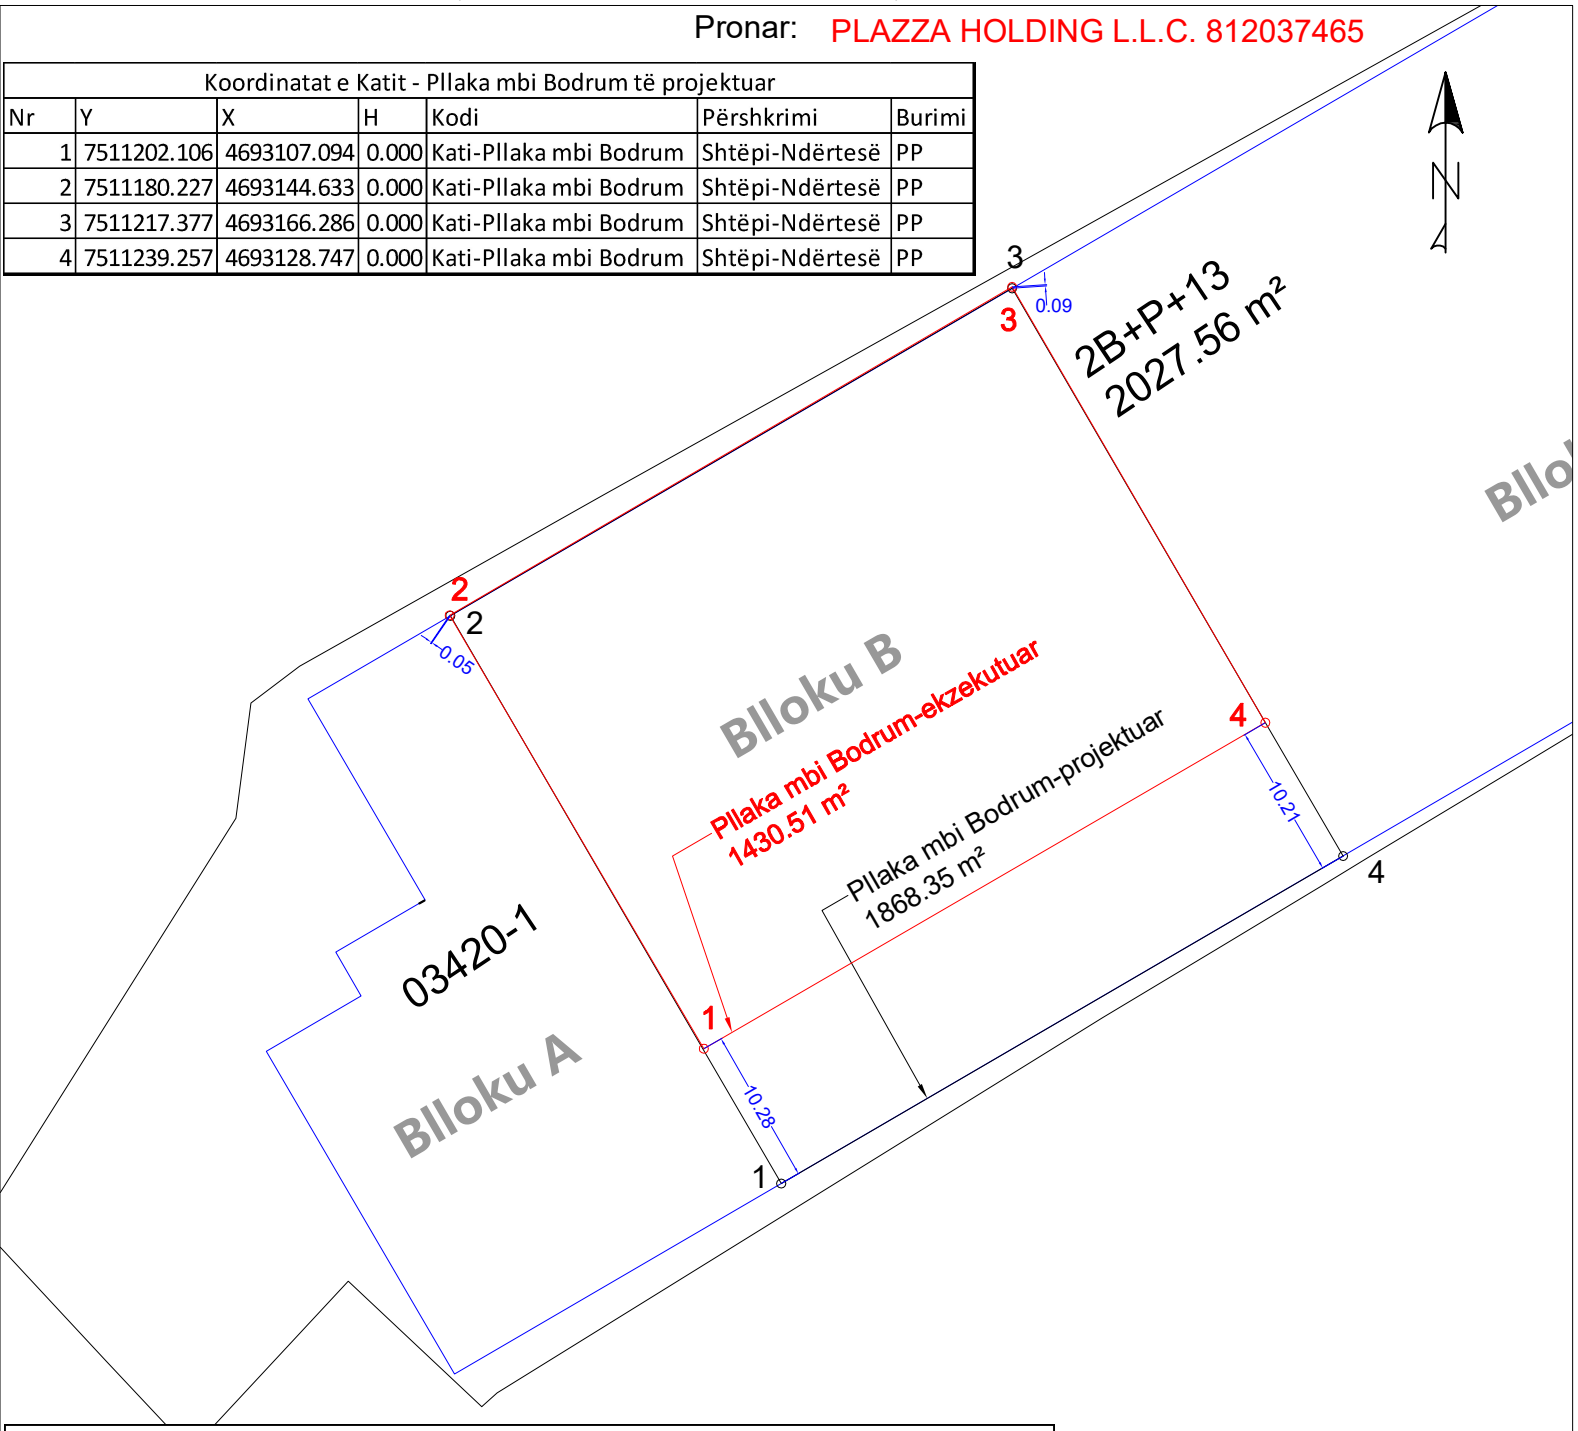

Koordinatat e Katit-Pllaka mbi Bodrum të ekzekutuar						
Nr	Y	X	H	Kodi	Përshkrimi	Burimi
1	7511196.988	4693116.012	623.782	Kati-Pllaka mbi Bodrum	Shtëpi-Ndërtesë	PM
2	7511180.184	4693144.662	623.823	Kati-Pllaka mbi Bodrum	Shtëpi-Ndërtesë	PM
3	7511217.371	4693166.378	623.827	Kati-Pllaka mbi Bodrum	Shtëpi-Ndërtesë	PM
4	7511234.116	4693137.564	623.807	Kati-Pllaka mbi Bodrum	Shtëpi-Ndërtesë	PM

Rilevoi / Snimio: Liridon Sejdiu

(emri dhe mbiemri i gjeodetit/kompanisë/ ime i prezime geodeta/ kompanije)

Etazha: Kati - Pllaka mbi Bodrum

Nr. i licencës / Br. licence: 140

V.V.

Nënshkrimi / Potpis:

Nënshkrimi / Potpis:

Data e rilevimit / Datum snimanja: 02/03/2026

Data e aprovimit / Datum usvajanja: