Zyra kadastrale komunale / Opštinska katastarska kancelarija: Ferizaj

Zona kadastrale / Katastarska zona: Ferizaj

Lloji i njësisë kadastrale / Vrsta katastarske jedinice : Situacion objektit

Nr. i njësisë kadastrale / Br. katastarske jedinice : 03420-1

Numri i lëndës / Broj predmeta:

Shkalla e zvoglimit / Razmera plana : 1:500

Republika e Kosovës

Republika Kosova-Republic of Kosova


Qeveria -Vlada-Government

Ministria e Mjedisit dhe Planifikimit Hapësinor /Ministarstvo Sredine i Prostornog Planiranja/Ministry of Environment and Spatial Planning

AGJENCIA KADASTRALE E KOSOVËS/ KATASTARSKA AGECIJA KOSOVA/ KOSOVA CADASTRAL AGENCY

Pronar: PLAZZA HOLDING L.L.C. 812037465

Koordinatat e Katit 2 të ekzekutuar						
Nr	Y	X	H	Kodi	Përshkrimi	Burimi
1	7511195.338	4693118.753	630.381	Kati 2	Shtëpi-Ndërtesë	PM
2	7511185.517	4693135.569	630.377	Kati 2	Shtëpi-Ndërtesë	PM
3	7511197.838	4693142.764	630.378	Kati 2	Shtëpi-Ndërtesë	PM
4	7511198.208	4693142.104	630.382	Kati 2	Shtëpi-Ndërtesë	PM
5	7511204.585	4693145.826	630.373	Kati 2	Shtëpi-Ndërtesë	PM
6	7511204.112	4693146.645	630.351	Kati 2	Shtëpi-Ndërtesë	PM
7	7511206.585	4693148.072	630.381	Kati 2	Shtëpi-Ndërtesë	PM
8	7511206.224	4693148.687	630.377	Kati 2	Shtëpi-Ndërtesë	PM
9	7511222.191	4693158.020	630.387	Kati 2	Shtëpi-Ndërtesë	PM
10	7511232.441	4693140.407	630.939	Kati 2	Shtëpi-Ndërtesë	PM

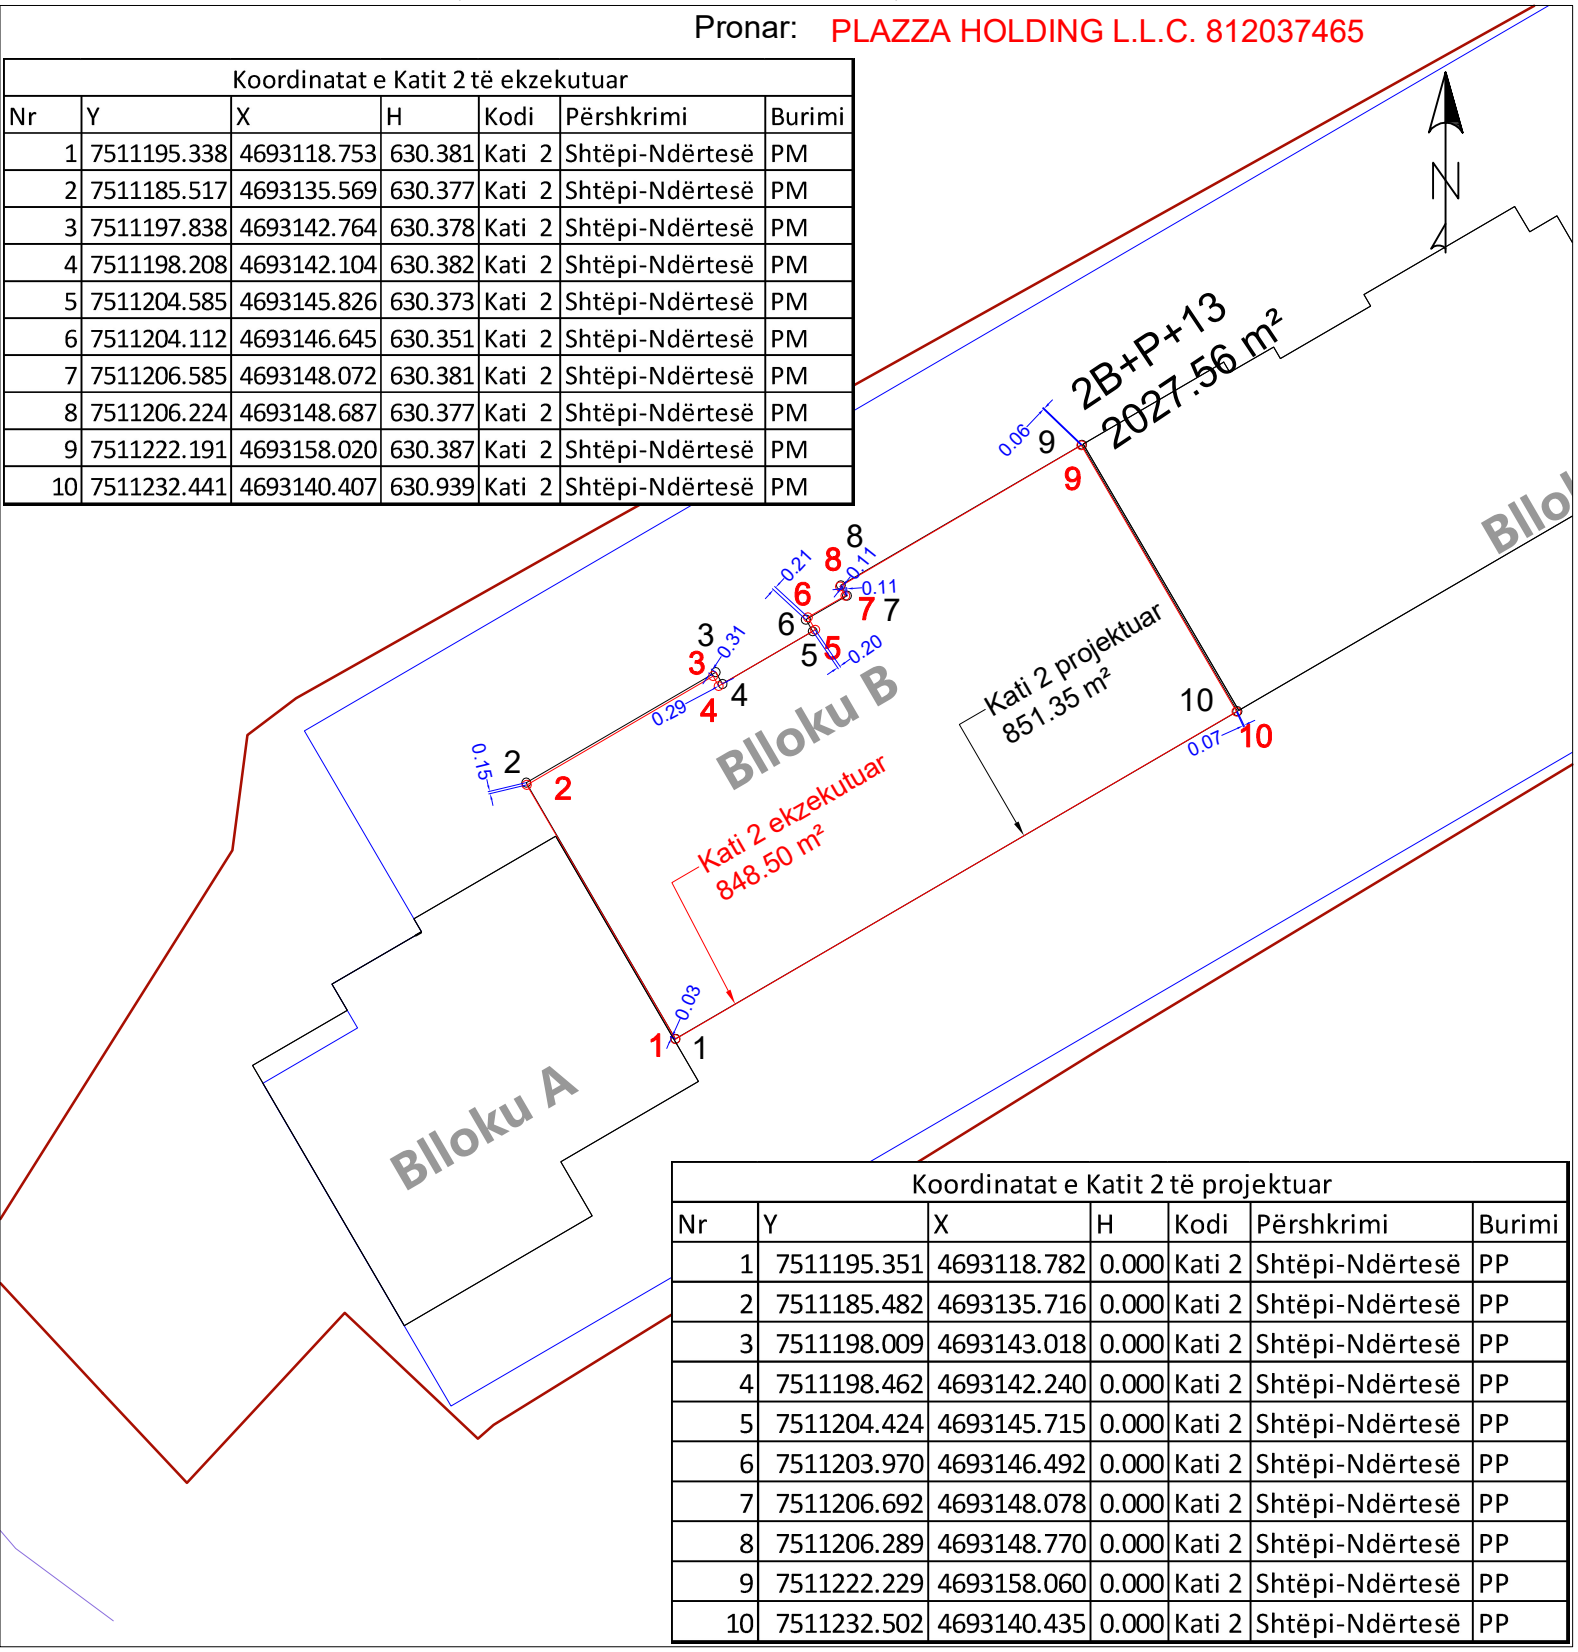

Koordinatat e Katit 2 të projektuar						
Nr	Y	X	H	Kodi	Përshkrimi	Burimi
1	7511195.351	4693118.782	0.000	Kati 2	Shtëpi-Ndërtesë	PP
2	7511185.482	4693135.716	0.000	Kati 2	Shtëpi-Ndërtesë	PP
3	7511198.009	4693143.018	0.000	Kati 2	Shtëpi-Ndërtesë	PP
4	7511198.462	4693142.240	0.000	Kati 2	Shtëpi-Ndërtesë	PP
5	7511204.424	4693145.715	0.000	Kati 2	Shtëpi-Ndërtesë	PP
6	7511203.970	4693146.492	0.000	Kati 2	Shtëpi-Ndërtesë	PP
7	7511206.692	4693148.078	0.000	Kati 2	Shtëpi-Ndërtesë	PP
8	7511206.289	4693148.770	0.000	Kati 2	Shtëpi-Ndërtesë	PP
9	7511222.229	4693158.060	0.000	Kati 2	Shtëpi-Ndërtesë	PP
10	7511232.502	4693140.435	0.000	Kati 2	Shtëpi-Ndërtesë	PP

Rilevoi / Snimio: Liridon Sejdiu

(emri dhe mbiemri i gjeodetit/kompanisë/ ime i prezime geodeta/ kompanije)

Nr. i licencës / Br. licence: 140

Nënshkrimi / Potpis:

Data e rilevimit / Datum snimanja: 10/08/2026

Etazha: Kati 2

V.V.

Nënshkrimi / Potpis:

Data e aprovimit / Datum usvajanja: